


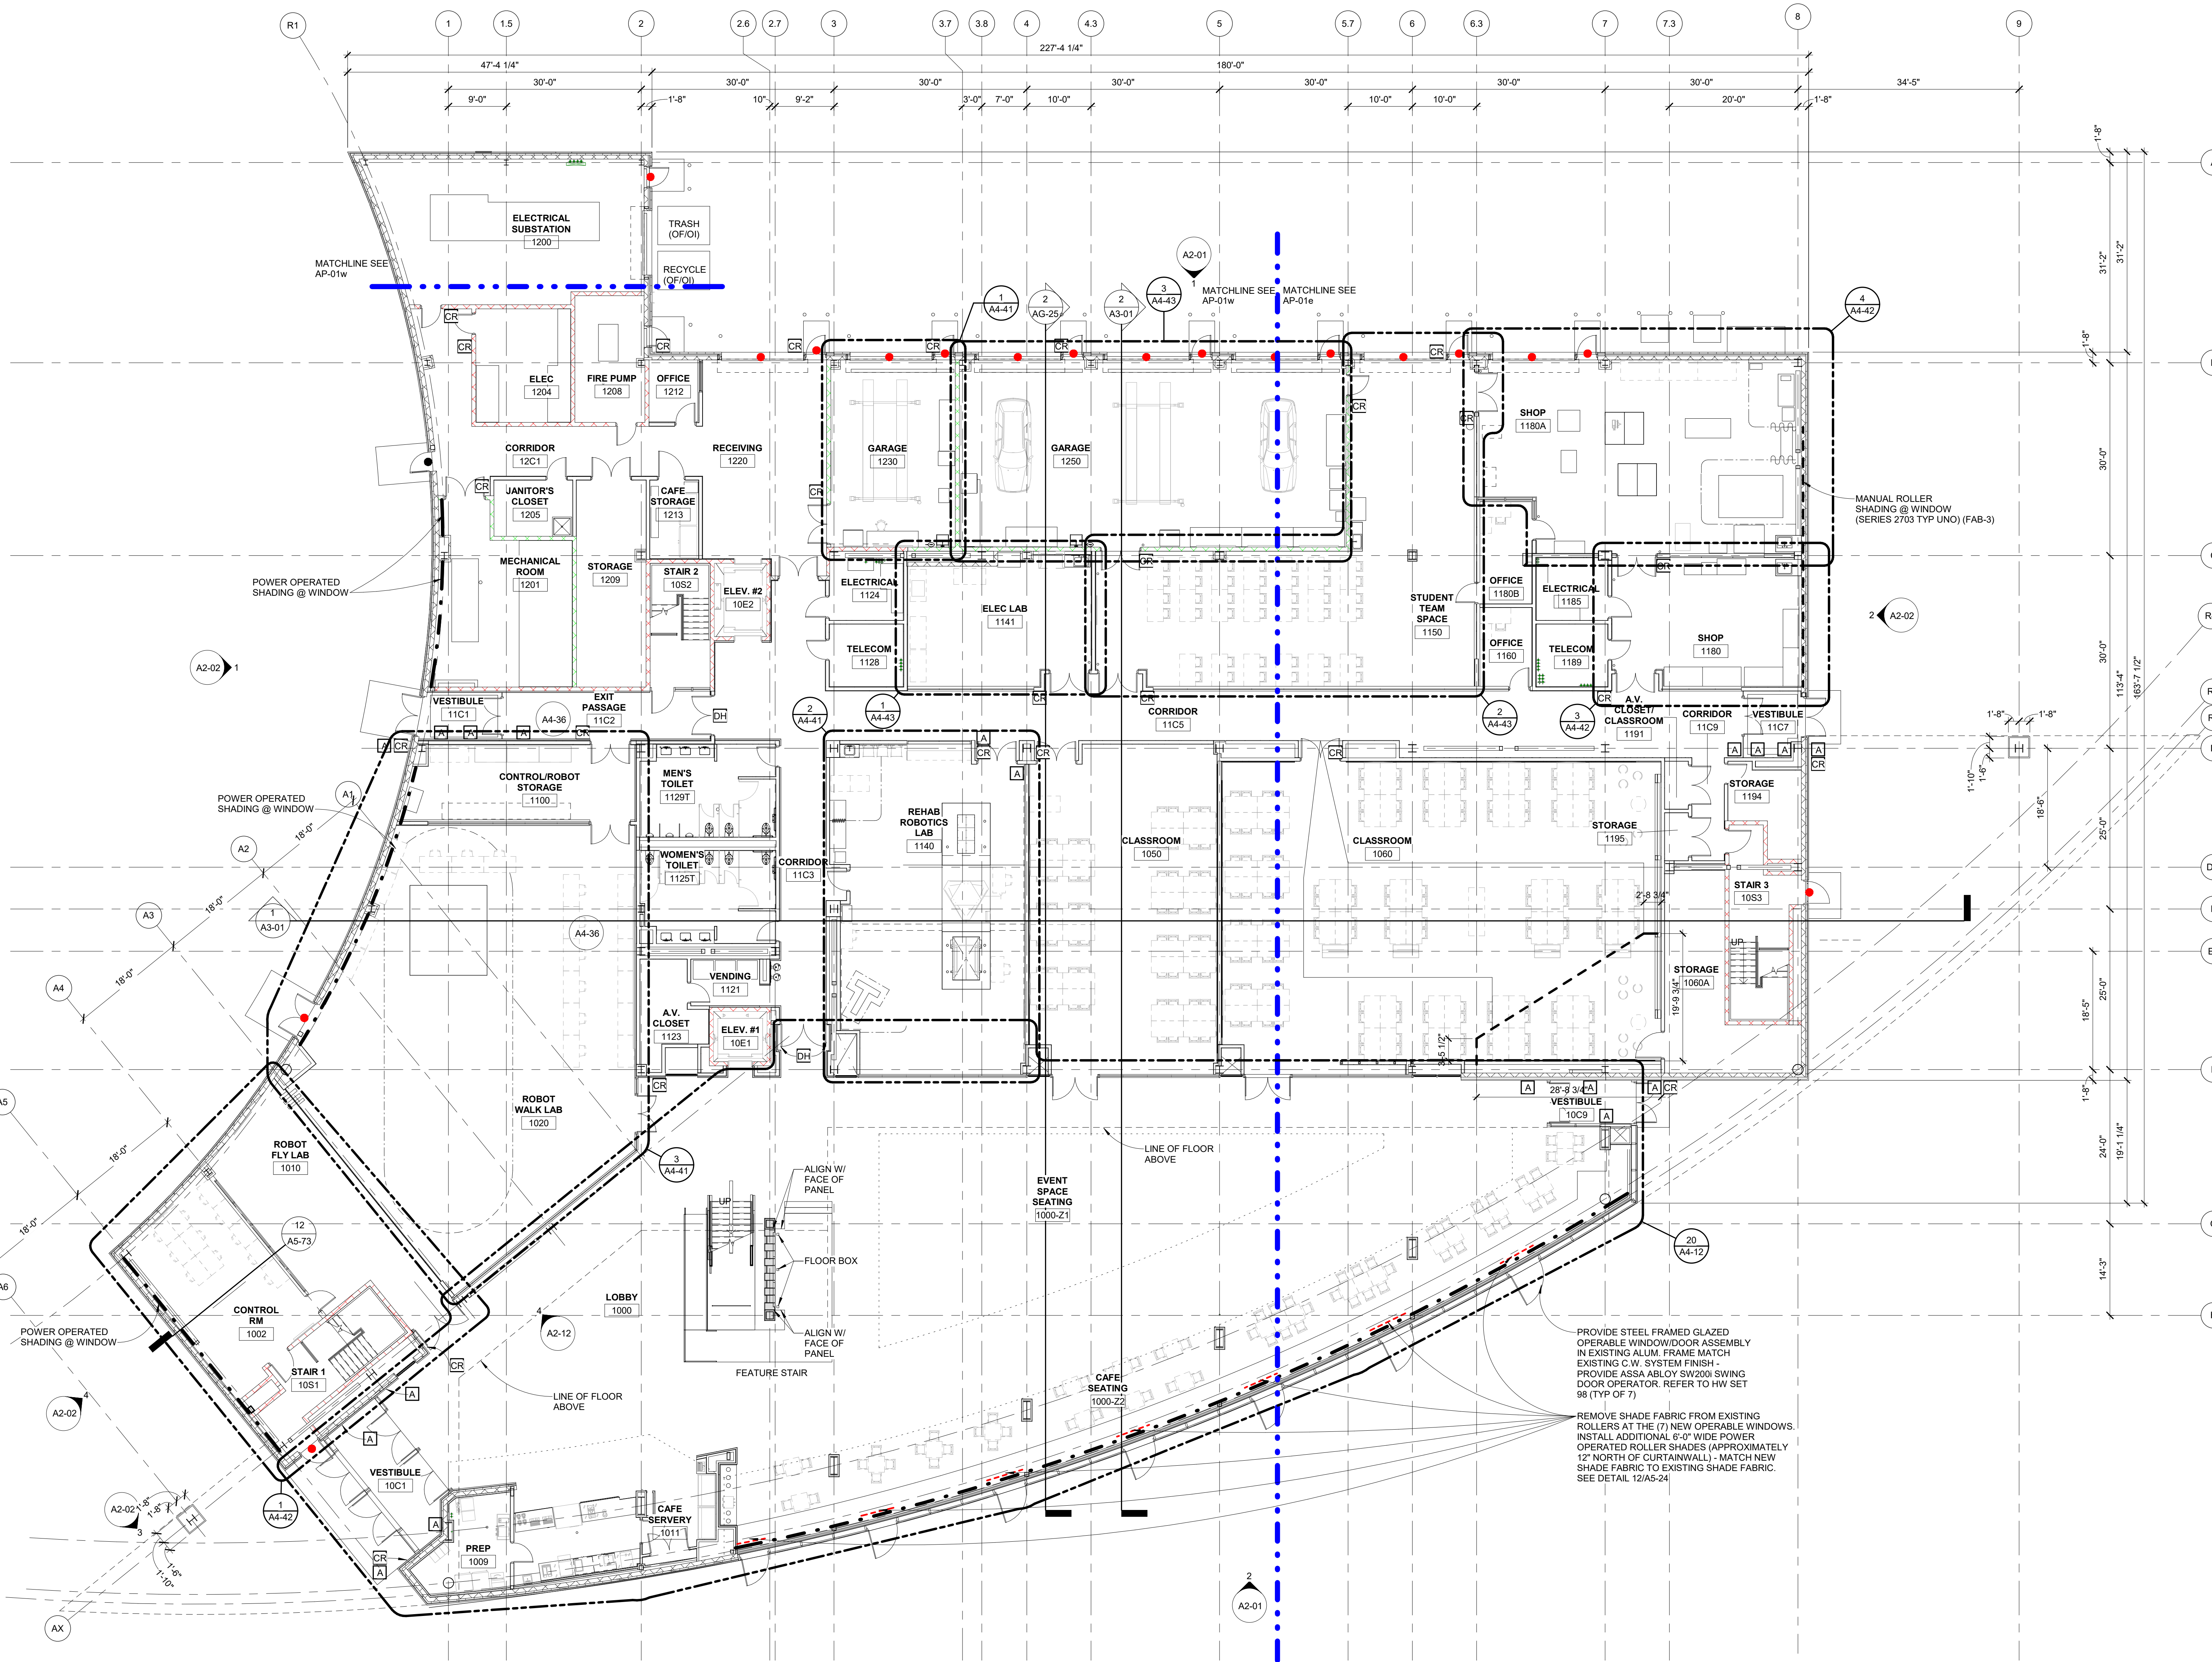

PROJECT GENERAL NOTES

- FIRST FLOOR LEVEL ELEVATION OF 100'-0" NOTED ON ARCHITECTURAL AND STRUCTURAL DRAWINGS EQUALS ELEVATION OF 888.30' NOTED ON CIVIL DRAWINGS. REFER TO SHEET AE-00 FOR BUILDING LOCATION & WORKPOINTS
- THE OWNER'S NORMAL OPERATIONS WILL BE CONTINUED DURING CONSTRUCTION. THE CONSTRUCTION SHALL NOT INTERFERE WITH THESE OPERATIONS IN ANY WAY WITHOUT THE OWNER'S EXPRESSED WRITTEN CONSENT.
- IT SHALL BE EACH TRADE CONTRACTORS RESPONSIBILITY TO VISIT THE SITE AND FAMILIARIZE THEMSELVES WITH ALL EXISTING CONDITIONS. EACH CONTRACTOR SHALL TAKE ALL NECESSARY FIELD MEASUREMENTS AND OTHERWISE VERIFY ALL DIMENSIONS AND EXISTING CONSTRUCTION CONDITIONS INDICATED AND/OR SHOWN ON THE DRAWINGS. SHOULD ANY ERROR OR INCONSISTENCY EXIST, THE CONTRACTOR SHALL NOT PROCEED WITH THE WORK AFFECTED THEREBY UNTIL REPORTING THE SAME TO THE ARCHITECT AND THE OWNER'S REPRESENTATIVE AND GETTING CLARIFICATION AND/OR CORRECTION.
- DIMENSIONS FOLLOWED BY +/- SHALL BE REVIEWED AND ALL NECESSARY ADJUSTMENTS MADE PRIOR TO FABRICATION AND/OR INSTALLATION OF WORK. CONTRACTOR SHALL NOTIFY ARCHITECT/ENGINEER OF ANY DISCREPANCIES BEFORE PROCEEDING WITH THE WORK.
- ALL EXISTING CONSTRUCTION AND SURFACES WHICH ARE TO REMAIN, BUT ARE AFFECTED BY THE WORK UNDER THIS CONTRACT SHALL BE RESTORED AND REFINISHED TO MATCH THE CONSTRUCTION, FINISH AND ALIGNMENT OF THE EXISTING ADJACENT CONSTRUCTION AND FINISHES.
- VERIFY QUANTITY, SIZE AND LOCATION OF ALL FLOOR, ROOF & WALL OPENINGS FOR MECHANICAL AND ELECTRICAL WORK WITH THE APPROPRIATE TRADE. PROVIDE ALL OPENINGS SHOWN OR REQUIRED FOR COMPLETION OF WORK.
- COORDINATE SIZE AND LOCATION OF ALL ACCESS PANELS WITH APPROPRIATE TRADES.
- COORDINATE SIZE AND LOCATION OF ALL HOUSE-KEEPING PADS AND/OR EQUIPMENT SUPPORTS WITH APPROPRIATE EQUIPMENT MANUFACTURER.
- PROVIDE POSITIVE SLOPE TO ALL FLOOR DRAINS WHILE KEEPING FLOOR LEVEL AT WALL BASE CONDITION.
- PROVIDE FIRE WATCH DURING FIELD CUTTING AND WELDING OPERATIONS, MEETING OWNERS REQUIREMENTS.
- PROVIDE WALL REINFORCEMENT TYPE 'A' PER DETAIL 7/A5-72. THESE LOCATIONS INCLUDE, BUT ARE NOT LIMITED TO: GRAB BARS, COUNTER SUPPORT BRACKETS, WALL CABINETS, BABY CHANGING STATIONS, WALL HUNG SHELVES & ITEMS WEIGHING MORE THAN 50 POUNDS.
- PROVIDE WALL REINFORCEMENT TYPE 'B' PER DETAIL 8/A5-72 AT ALL OTHER LOCATIONS REQUIRING WALL REINFORCEMENT NOTED IN THE TOILET ACCESSORY SCHEDULE & THE DRAWINGS.
- THE EXTENT OF HATCHING ON DRAWINGS IS ONLY SUFFICIENT TO INDICATE THE NATURE OF THE CONSTRUCTION OR MATERIALS. TERMINATION OF THE HATCHING SHALL NOT BE CONSTRUED TO REPRESENT A CHANGE OR TERMINATION OF MATERIAL.
- NOT USED.
- THE CONTRACTOR SHALL VERIFY THE EXISTENCE, LOCATION & ELEVATION OF ALL UNDERGROUND UTILITIES IN WORK AREAS PRIOR TO PROCEEDING WITH CONSTRUCTION. ALL DISCREPANCIES SHALL BE DOCUMENTED AND FORWARDED TO ARCHITECT AND OWNERS REPRESENTATIVE FOR ACTION.
- IT IS THE CONTRACTORS RESPONSIBILITY TO INVESTIGATE FIELD CONDITIONS AND PROVIDE AS NEEDED TEMPORARY SUPPORTS, SHORING AND / OR PROTECTION OF EXISTING STRUCTURES AND UNDERGROUND UTILITIES DURING EXECUTION OF WORK.
- ALL WORK TO CONFORM TO THE REQUIREMENTS OF THE LOCAL AND STATE CODES. COORDINATE W/ SPECIFICATIONS, DIVISION 1.
- RELEVANT DIMENSIONS AND ELEVATIONS FOR EQUIPMENT INSTALLATIONS SHALL BE VERIFIED AGAINST MANUFACTURERS CERTIFIED EQUIPMENT DRAWINGS.
- CONTRACTOR SHALL PROVIDE TEMPORARY DUST PROOF PARTITIONS AS REQUIRED, OR WHERE REQUESTED BY OWNER'S REPRESENTATIVE. PARTITIONS SHALL BE FIRE RATED WHERE REQUIRED BY CODE HAVING JURISDICTION. ALL TEMPORARY PARTITIONS SHALL BE CONSTRUCTED IN A MANNER AND OF MATERIALS OFFERING ADEQUATE PROTECTION TO OWNER'S EQUIPMENT AND PERSONNEL.
- DO NOT SCALE DRAWINGS TO DETERMINE SIZES AND DIMENSIONS. USE FIGURED DIMENSIONS ONLY. DIMENSIONS ARE TO FINISHED FACE OF WALLS UNLESS OTHERWISE NOTED. ALL PERIMETER DIMENSIONS ARE FROM FACE OF PERIMETER WALLS.
- ALL PENETRATIONS TO FLOORS, CEILINGS AND WALLS SHALL BE SEALED AND FIRE STOPPED TO A FIRE RATING EQUAL TO THE CONSTRUCTION BEING PENETRATED.
- NEW WORK SHALL ALIGN WITH AND MATCH EXISTING WORK UNLESS OTHERWISE NOTED.

FLOOR PLAN LEGEND

- | | |
|---|--|
| COL | NEW COLUMN LINE |
| XXXX | INDICATES ROOM NUMBER SUFFIX DENOTES NUMBER OF ADDITIONAL DOOR IN ROOM |
| NEW DOOR | NEW DOOR |
| XXXX | TYP (U.O.N.) |
| (X'-X" T.O. WALL WHERE SHOWN, DEVIATE FROM PARTITION TYPE - SEE SHEETS A5-71 & A5-72) | |
| ROOM NAME XXXX | ROOM NAME & NUMBER |
| ○ | FLOOR SINK (FS) |
| □ | FLOOR DRAIN (FD) |
| ▨ | TRENCH DRAIN (TD) |
| ● | DOOR CONTACT |
| A | AUTOMATIC OPERATOR |
| CR | CARD READER |
| DH | DOOR HOLD OPEN |
| --- | REINFORCEMENT |
| ↑ | MASONRY C.J. REFER TO A5-72 |
| ○ | EQUIPMENT REFER TO SHEET A4-47 |
| TP | TOUCH PANEL @ 48" A.F.F. TYP. |
| ⬇ | POWER & DATA @ 18" A.F.F. (U.N.O.) |
| —R.S. | ROOM SCHEDULER SEE DETAIL 27/A5-81 |

N
COMPOSITE FIRST FLOOR PLAN
SCALE: 3/32" = 1'-0"



College of
Engineering &
Office of Research

503 Thompson Street
Ann Arbor,
Michigan 48109-1340

Ford Motor
Company Robotics
Building

2505 Hayward Street
Ann Arbor,
Michigan 48109-1340 North Campus

Date	Issued For
04/24/2017	DD Review
09/20/2017	95% Owner Review
12/18/2017	Bids
03/28/2018	Construction Set
10/26/2018	ASI 09
04/29/2019	ASI 18
08/13/2019	ASI 25
10/09/2019	ASI 31
11/20/2019	ASI 35
01/10/2020	ASI 39
01/16/2020	ASI 38
08/18/2020	ASI 45
09/21/2020	ASI 45.1 Post Bld Addendum 2
05/21/2021	For Record

HED

26913 Northwestern Hwy
Suite 200
Southfield, Michigan
48033 USA

(248) 262-1500
WWW.HED.DESIGN

2013-10079-000
UM # P-00007306

First Floor
Composite Plan

AC-01



UNIVERSITY OF MICHIGAN


College of Engineering & Office of Research

503 Thompson Street
Ann Arbor, Michigan 48109-1340

Ford Motor Company Robotics Building

2505 Hayward Street
Ann Arbor, Michigan 48109-1340 North Campus

Date Issued For
04/24/2017 DD Review
09/20/2017 95% Owner Review
12/18/2017 Bid
03/28/2018 Construction Set
10/26/2018 ASI 09
04/29/2019 ASI 18
09/30/2019 ASI 30
10/09/2019 ASI 32
05/21/2021 For Record

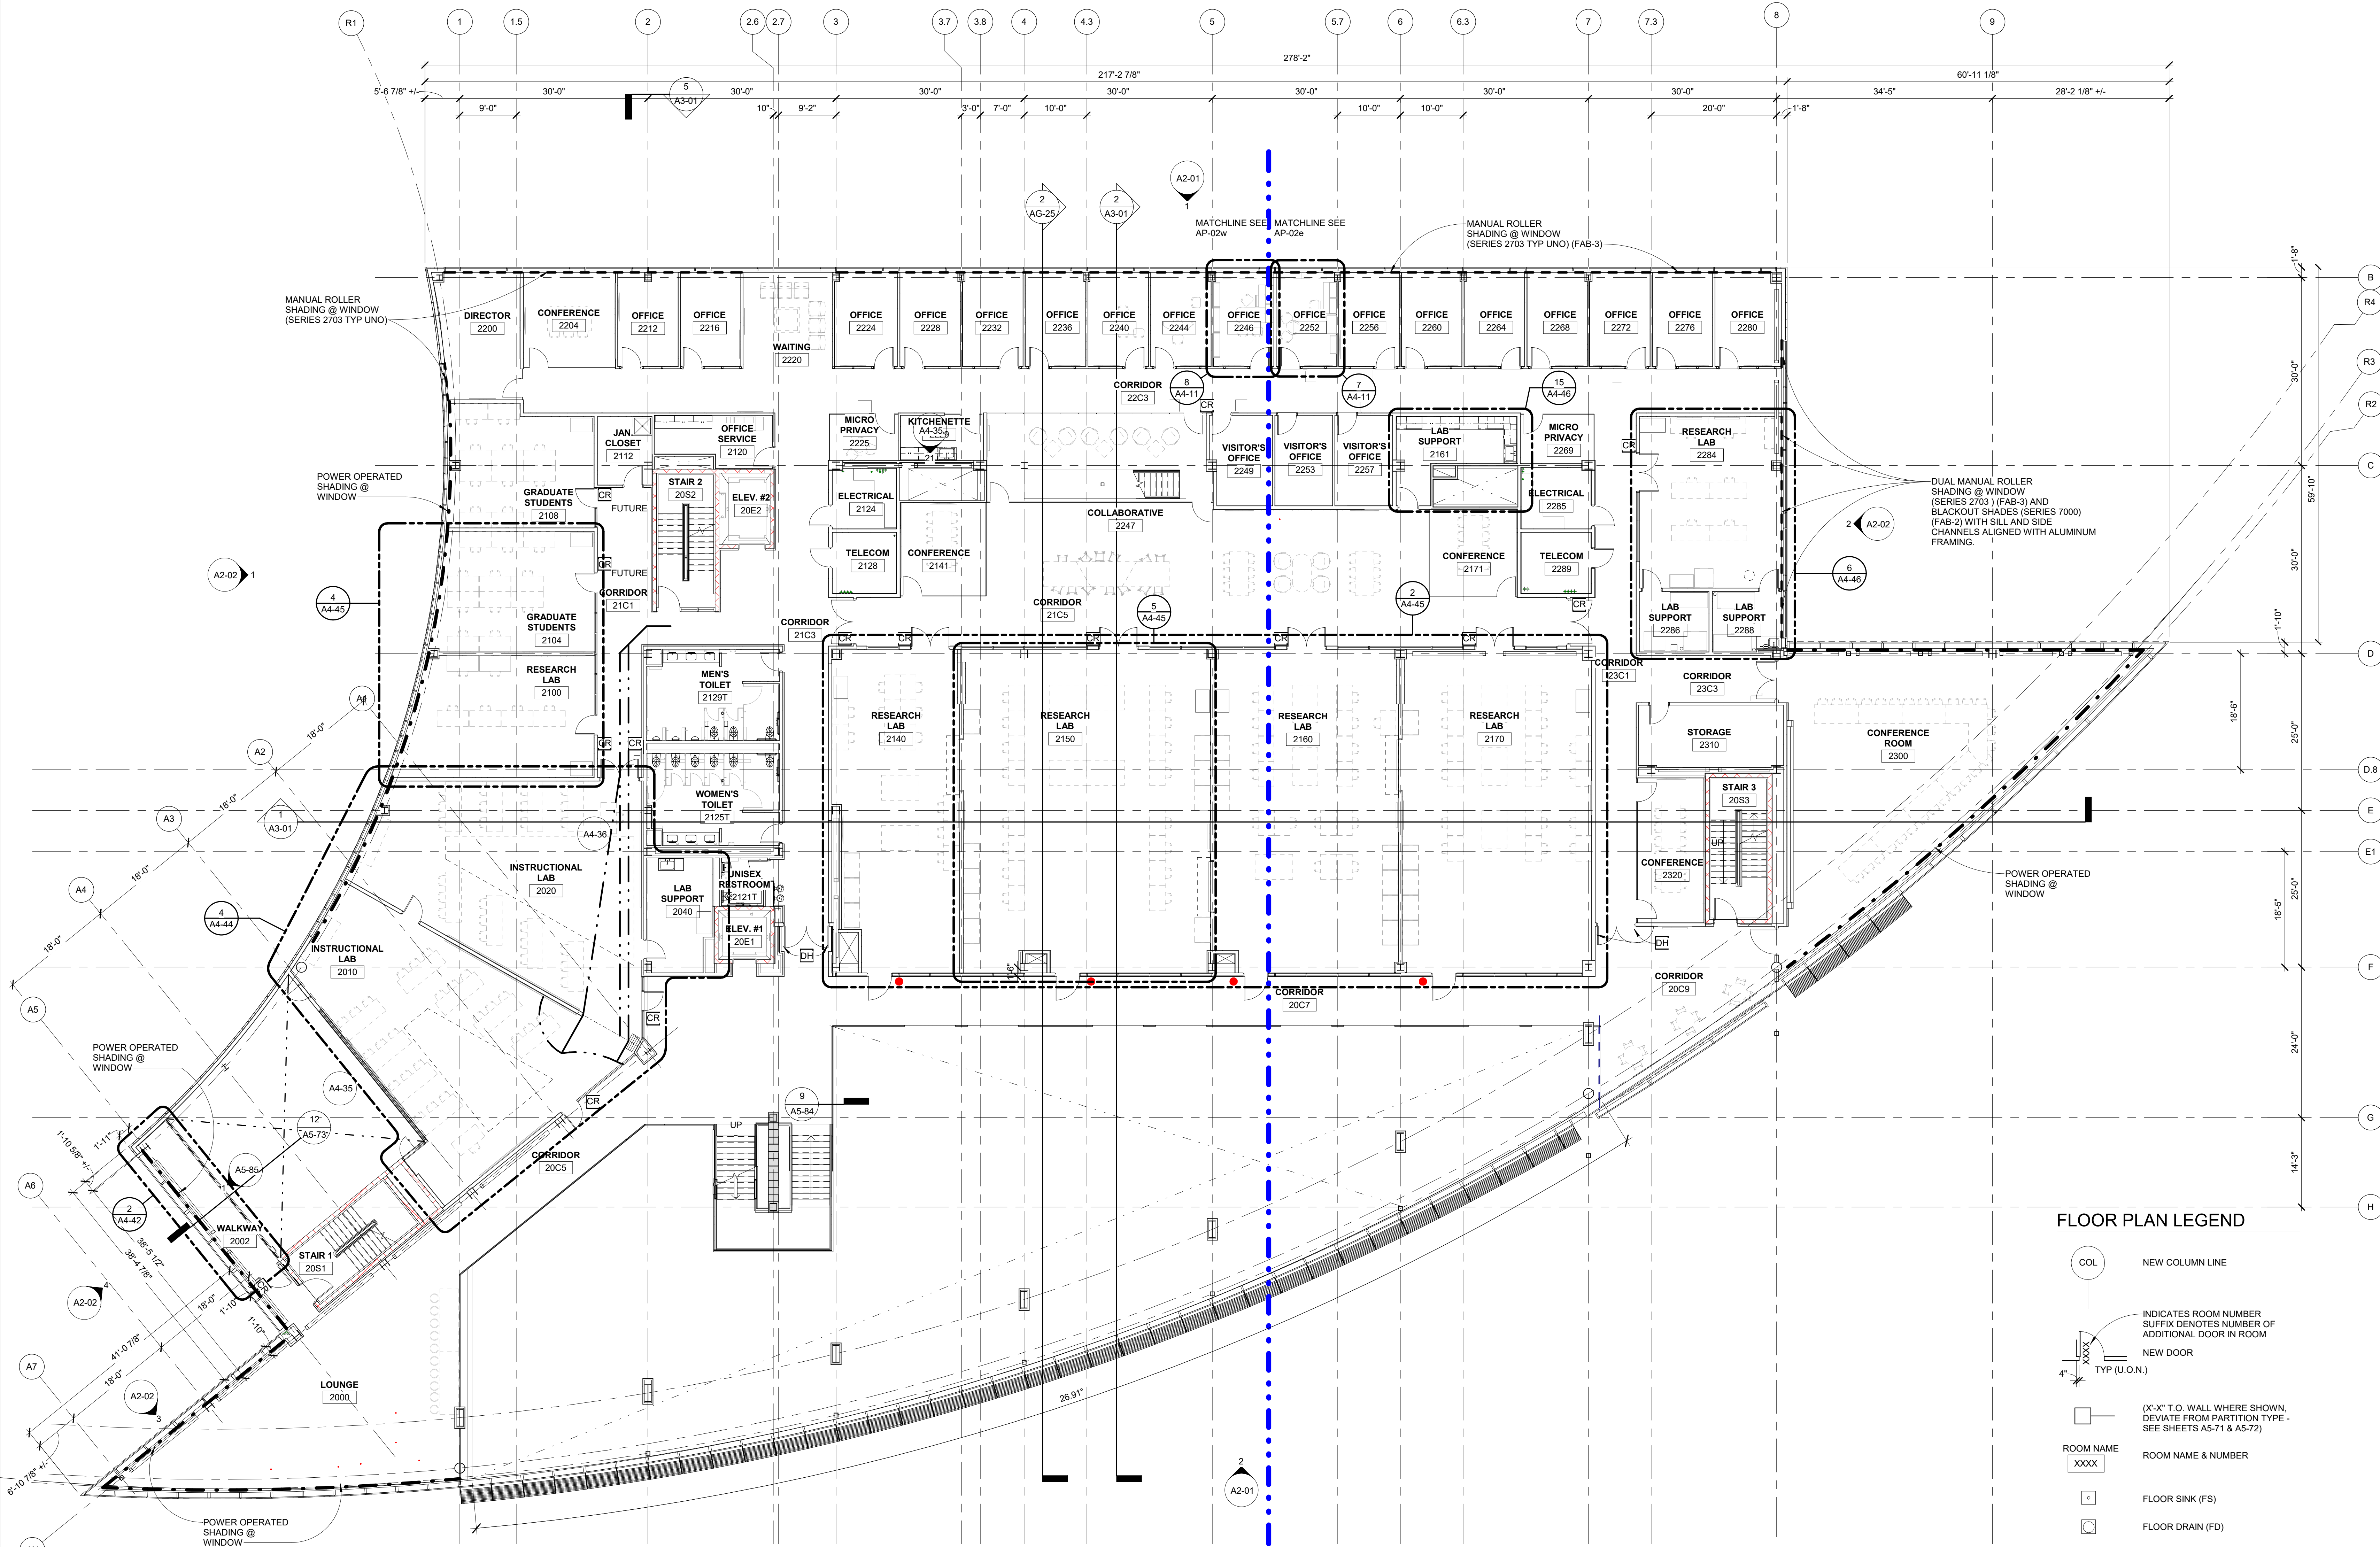

COMPOSITE SECOND FLOOR PLAN
SCALE: 3/32" = 1'-0"

FLOOR PLAN LEGEND

- COL NEW COLUMN LINE
- INDICATES ROOM NUMBER SUFFIX DENOTES NUMBER OF ADDITIONAL DOOR IN ROOM
- NEW DOOR
- TYP (U.O.N.)
- (X'-X" T.O. WALL WHERE SHOWN, DEVIATE FROM PARTITION TYPE - SEE SHEETS A5-71 & A5-72)
- ROOM NAME XXXX
- ROOM NAME & NUMBER
- FLOOR SINK (FS)
- FLOOR DRAIN (FD)
- TRENCH DRAIN (TD)
- DOOR CONTACT
- AUTOMATIC OPERATOR
- CARD READER
- DOOR HOLD OPEN
- REINFORCEMENT
- MASONRY C.J. REFER TO A5-72
- EQUIPMENT REFER TO SHEET A4-47
- TOUCH PANEL @ 48" A.F.F. TYP
- POWER & DATA @ 16" A.F.F. (U.O.)
- R.S. ROOM SCHEDULER SEE DETAIL 27/A5-61


HED

26913 Northwestern Hwy
Suite 200
Southfield, Michigan
48033 USA
(248) 262-1500
WWW.HED.DESIGN

2013-10079-000
UM # P-00007306

Second Floor Composite Plan

AC-02

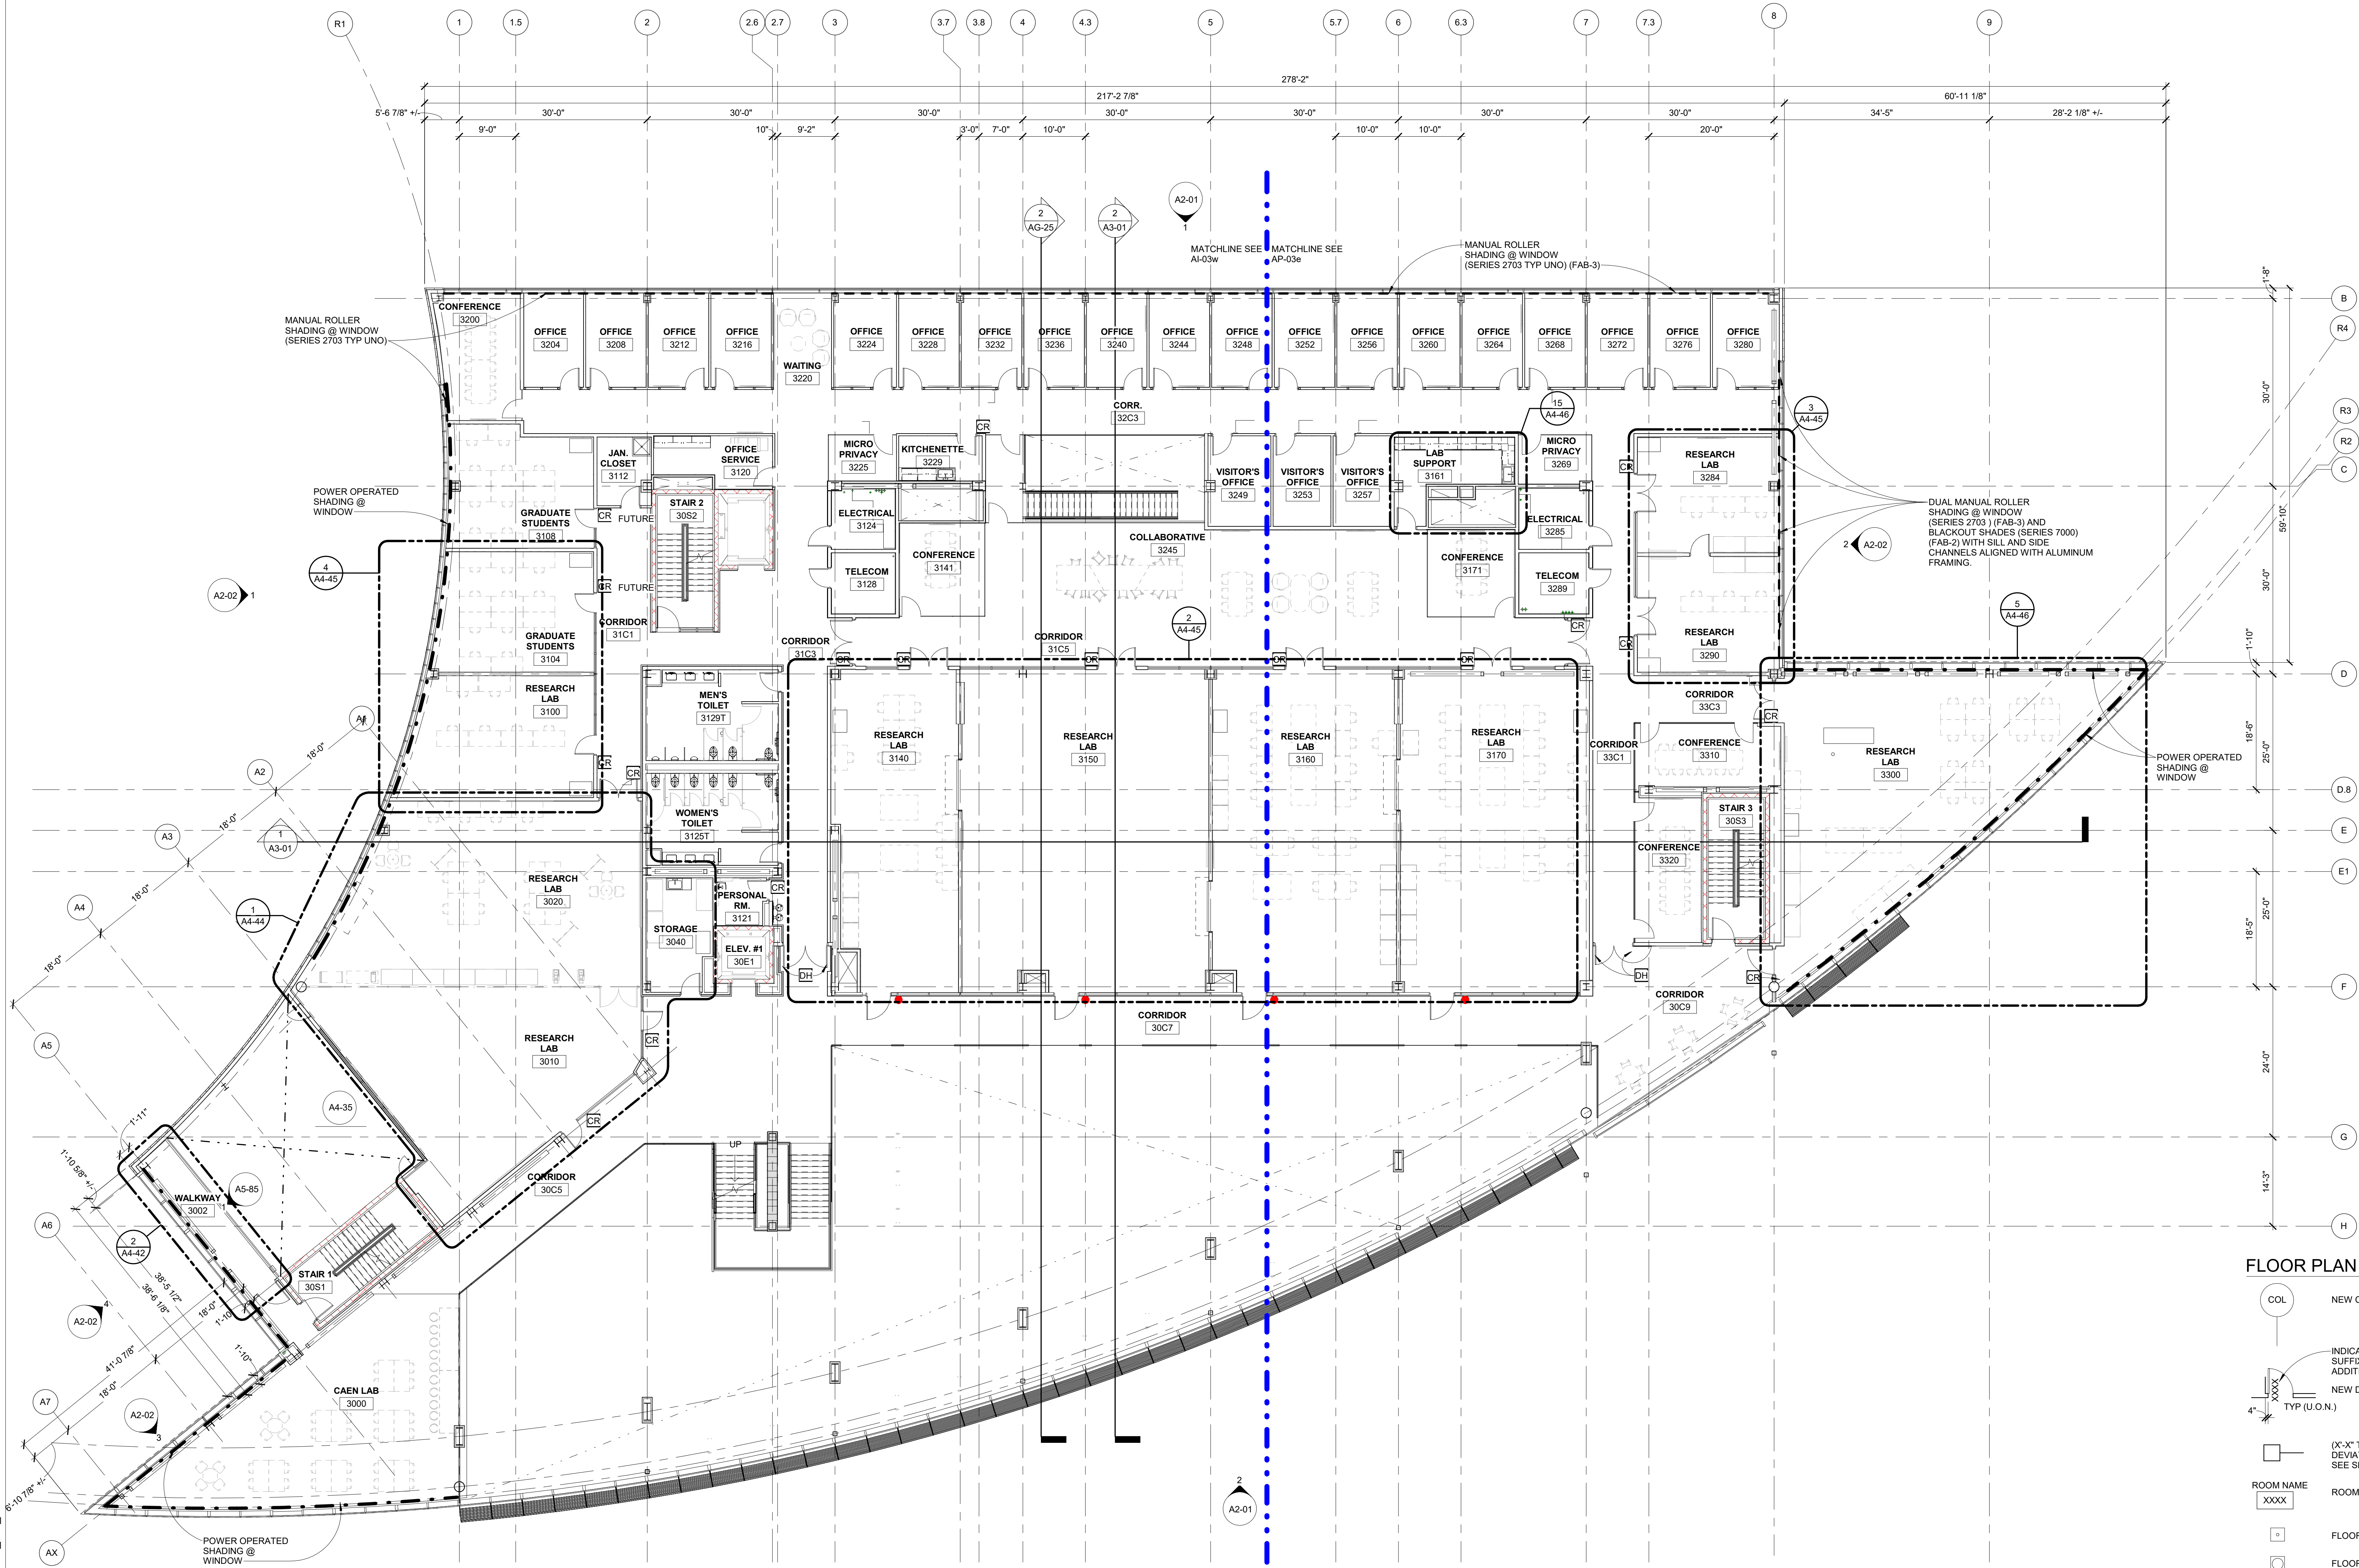

COMPOSITE THIRD FLOOR PLAN
SCALE: 3/32" = 1'-0"

FLOOR PLAN LEGEND

- COL NEW COLUMN LINE
- INDICATES ROOM NUMBER
SUFFIX DENOTES NUMBER OF
ADDITIONAL DOOR IN ROOM
- NEW DOOR
TYP (U.O.N.)
- (X'-X" T.O. WALL WHERE SHOWN,
DEVIATE FROM PARTITION TYPE -
SEE SHEETS A5-71 & A5-72)
- ROOM NAME
XXXX ROOM NAME & NUMBER
- FLOOR SINK (FS)
- FLOOR DRAIN (FD)
- TRENCH DRAIN (TD)
- DOOR CONTACT
- AUTOMATIC OPERATOR
- CR CARD READER
- DOOR HOLD OPEN
- REINFORCEMENT
MASONRY C.J. REFER
TO A5-72
- EQUIPMENT REFER
TO SHEET A4-47
- TP TOUCH PANEL @
48" A.F.F. TYP.
- POWER & DATA @
16" A.F.F. (U.O.)
- R.S. ROOM SCHEDULER
SEE DETAIL 27A5-61



UNIVERSITY OF
MICHIGAN

College of
Engineering &
Office of Research

503 Thompson Street
Ann Arbor,
Michigan 48109-1340

Ford Motor
Company Robotics
Building

2505 Hayward Street
Ann Arbor,
Michigan 48109-1340 North Campus

Date Issued For
04/24/2017 DD Review
09/20/2017 95% Owner Review
12/18/2017 Bus
02/05/2018 Addendum No. 4
03/28/2018 Construction Set
10/26/2018 ASI 09
04/29/2019 ASI 18
11/20/2019 ASI 35
01/16/2020 ASI 38
05/21/2021 For Record




26913 Northwestern Hwy
Suite 200
Southfield, Michigan
48033 USA
(248) 262-1500
WWW.HED.DESIGN

2013-10079-000
UM # P-00007306

Third Floor
Composite Plans

AC-03

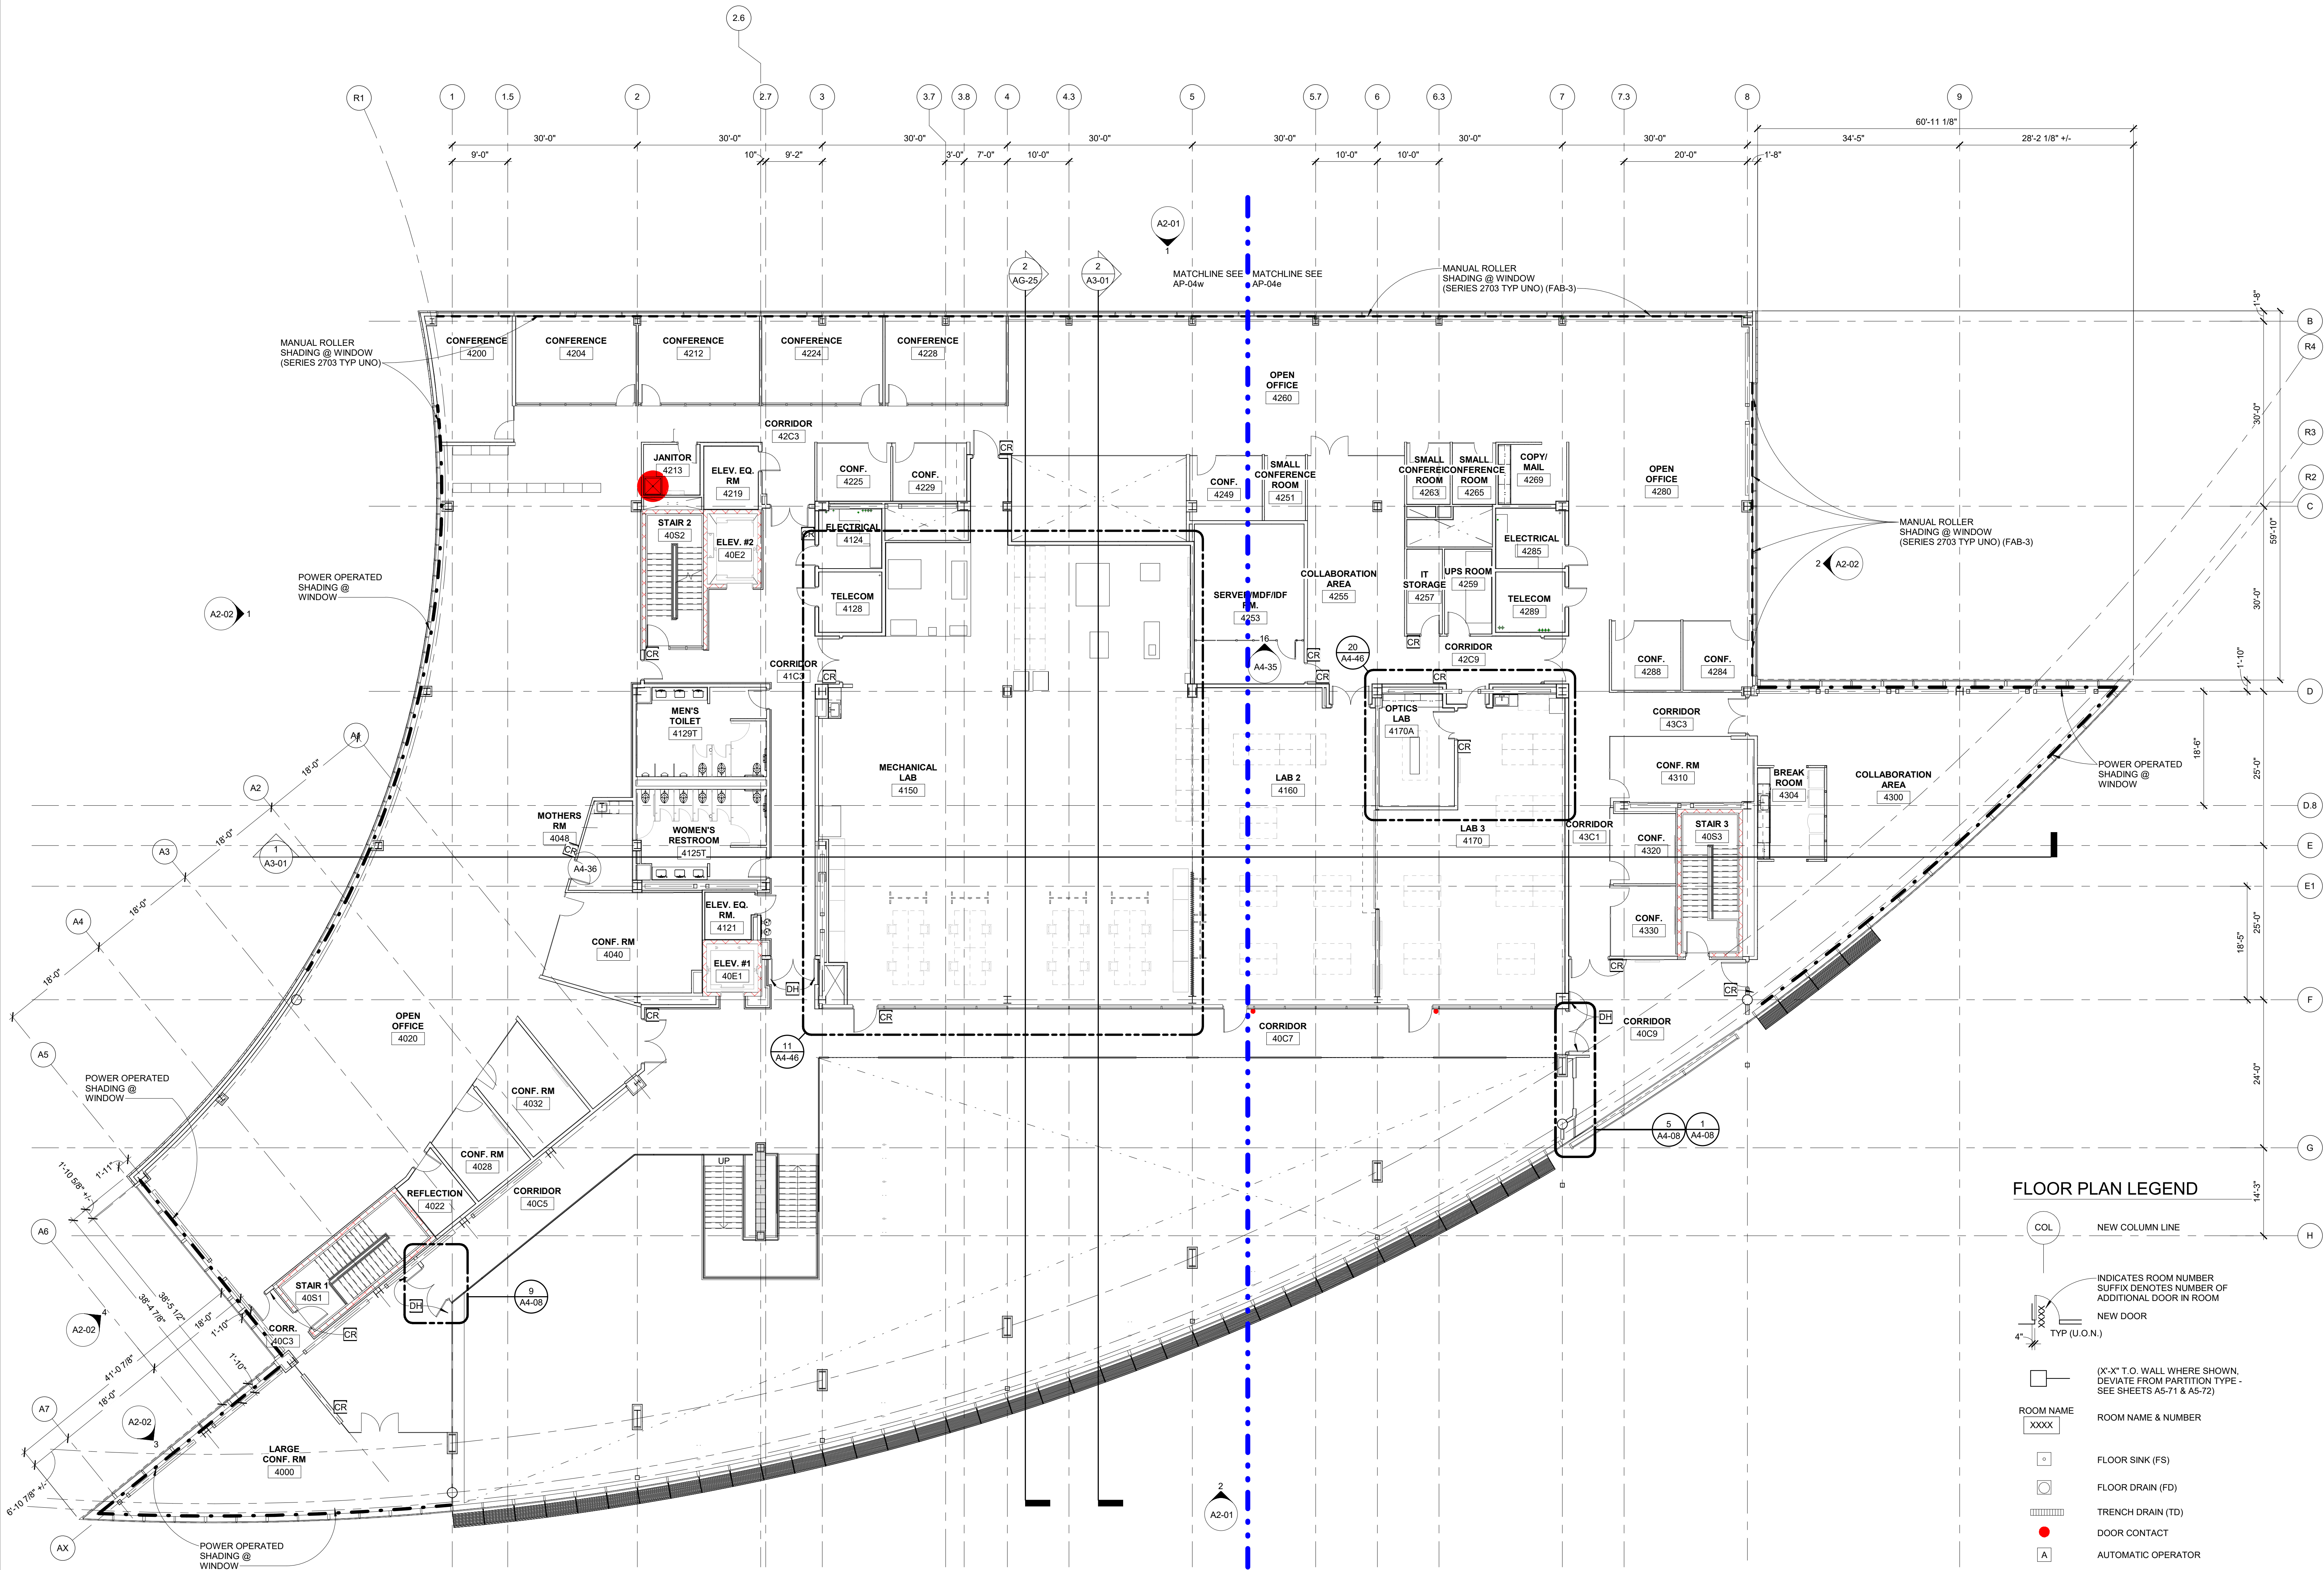

FLOOR PLAN LEGEND

- COL NEW COLUMN LINE
- INDICATES ROOM NUMBER
SUFFIX DENOTES NUMBER OF
ADDITIONAL DOOR IN ROOM
- NEW DOOR
TYP (U.O.N.)
- (X-X) T.O. WALL WHERE SHOWN,
DEVIATE FROM PARTITION TYPE -
SEE SHEETS A5-71 & A5-72
- ROOM NAME
XXXX ROOM NAME & NUMBER
- FLOOR SINK (FS)
- FLOOR DRAIN (FD)
- TRENCH DRAIN (TD)
- DOOR CONTACT
- AUTOMATIC OPERATOR
- CARD READER
- DOOR HOLD OPEN
- REINFORCEMENT
MASONRY C.J. REFER
TO A5-72
- EQUIPMENT REFER
TO SHEET A4-47
- TP TOUCH PANEL @
48" A.F.F. TYP.
- POWER & DATA @
16" A.F.F. (U.N.O.)
- R.S. ROOM SCHEDULER
SEE DETAIL 27/A5-61

N
COMPOSITE FOURTH FLOOR PLAN
SCALE: 3/32" = 1'-0"



UNIVERSITY OF
MICHIGAN

College of
Engineering &
Office of Research

503 Thompson Street
Ann Arbor,
Michigan 48109-1340

Ford Motor
Company Robotics
Building

2505 Hayward Street
Ann Arbor,
Michigan 48109-1340 North Campus

Date Issued For
04/24/2017 DD Review
09/20/2017 95% Owner Review
12/18/2017 Bid
03/28/2018 Construction Set
10/26/2018 ASI 09
03/12/2019 ASI 15
04/28/2019 ASI 18
09/10/2019 ASI 27
08/18/2020 ASI 45
05/21/2021 For Record



26913 Northwestern Hwy
Suite 200
Southfield, Michigan
48033 USA
(248) 262-1500
WWW.HED.DESIGN

© 2017
2013-10079-000
UM # P-00007306

Fourth Floor
Composite Plan

AC-04